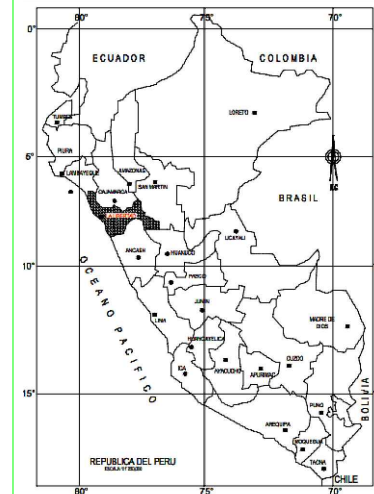
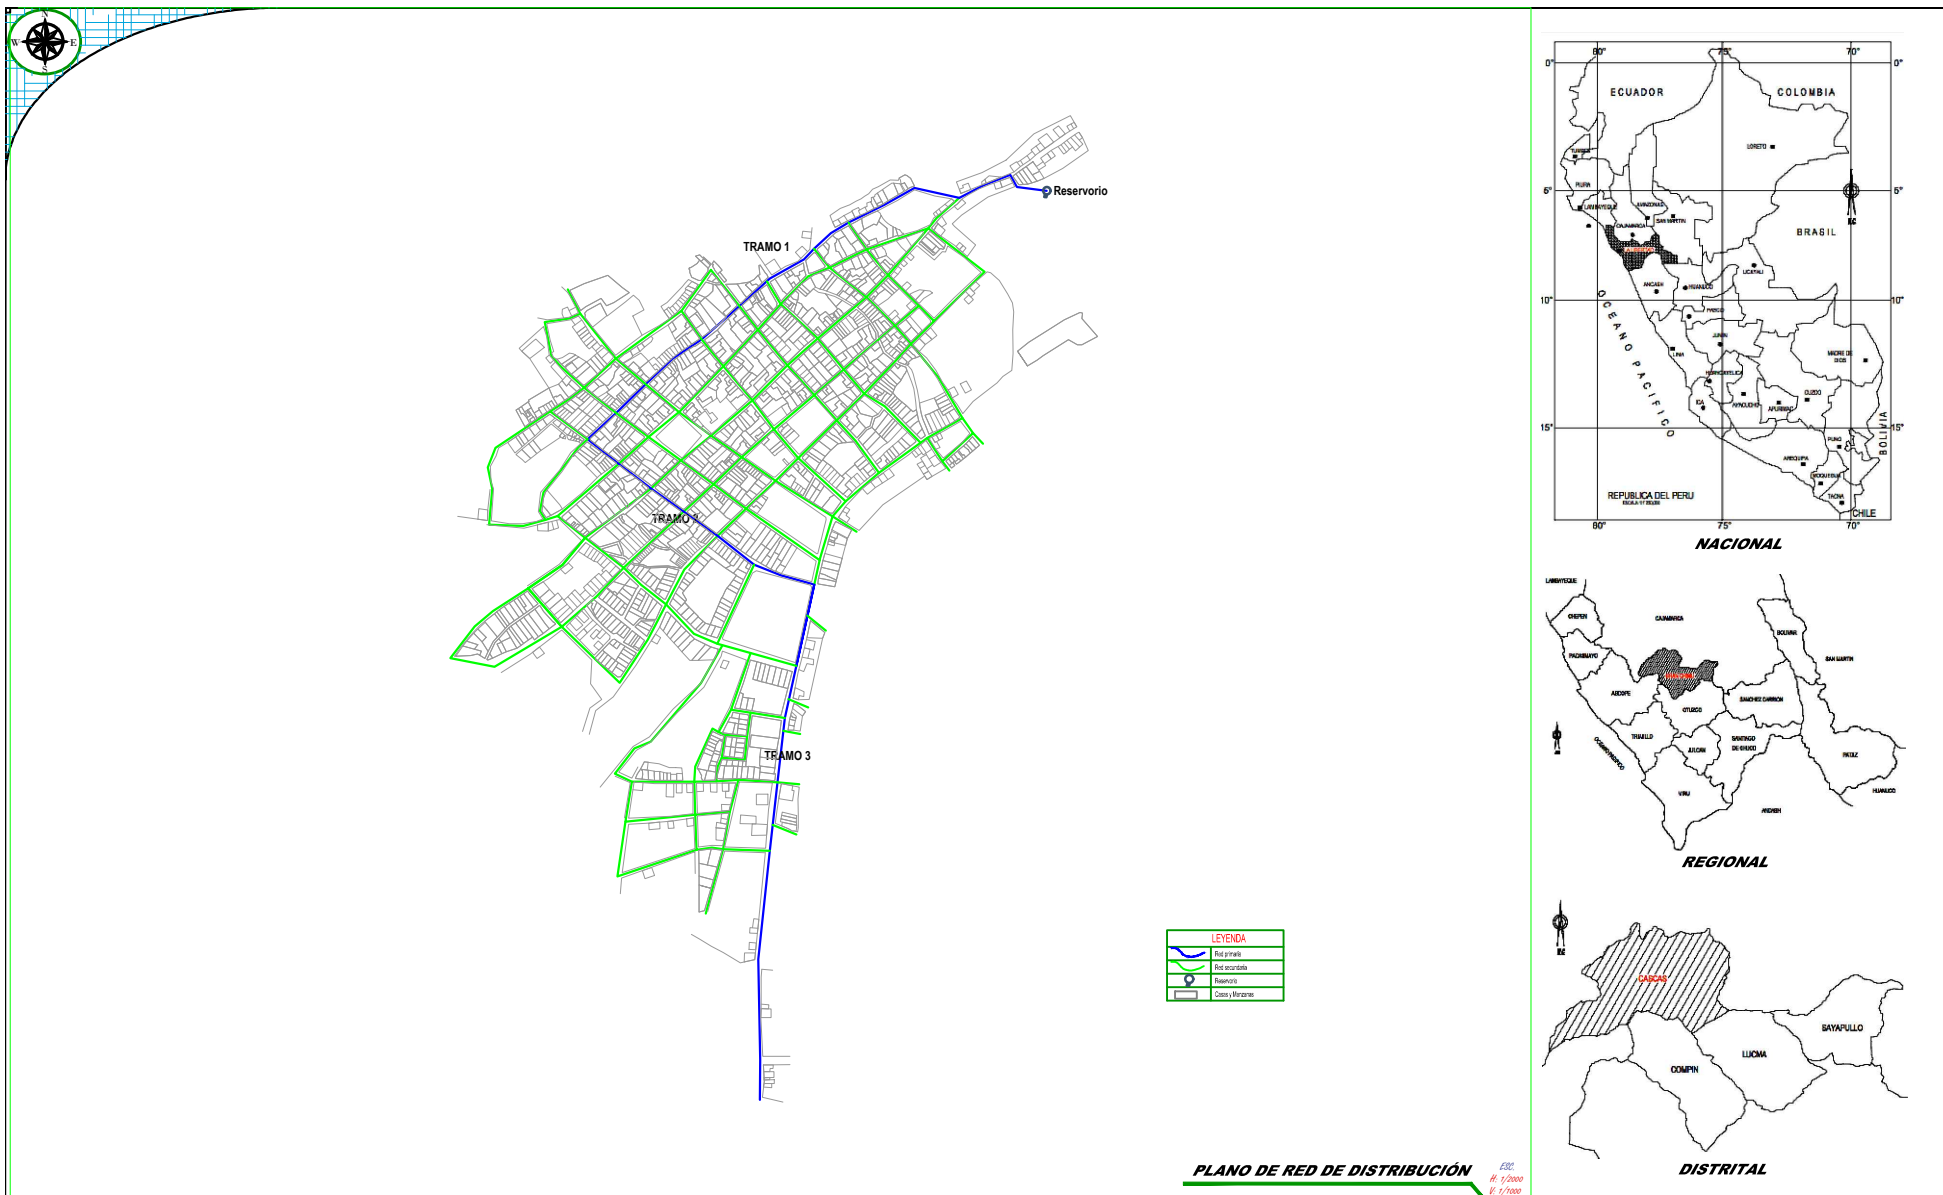


UNIVERSIDAD DE INGENIERÍA
Y TECNOLOGÍA
CICLO 2026-1

PROYECTO:
"AMPLIACIÓN Y MEJORAMIENTO DE LOS SISTEMAS DE AGUA POTABLE Y ALCANTARILLADO DE LA LOCALIDAD DE CASCAS"

PROYECTISTA:

DIBUJO Y DISEÑO:

R.A.H.H.

REVISÓ: J.J.R.C.

APRUEBA: J.J.R.C.

PLANO:
RED DE DISTRIBUCIÓN

REGION: LA LIBERTAD
PROVINCIA: GRAN CHIMU
DISTRITO: CASCAS

ESCALA: 1:4000

LÁMINA:
PD-01